



BIM 360://028-152 - 2020 KPMC - KPMC Campus Projects/1152133-AR-CHINO-MOB-RESTORATION.rvt
7/20/2021 3:58:18 PM

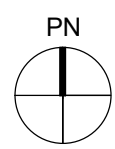

EQUIPMENT PLAN - SEGMENT - FLOOR 1 - DEPENDENT
1/4" = 1'-0"

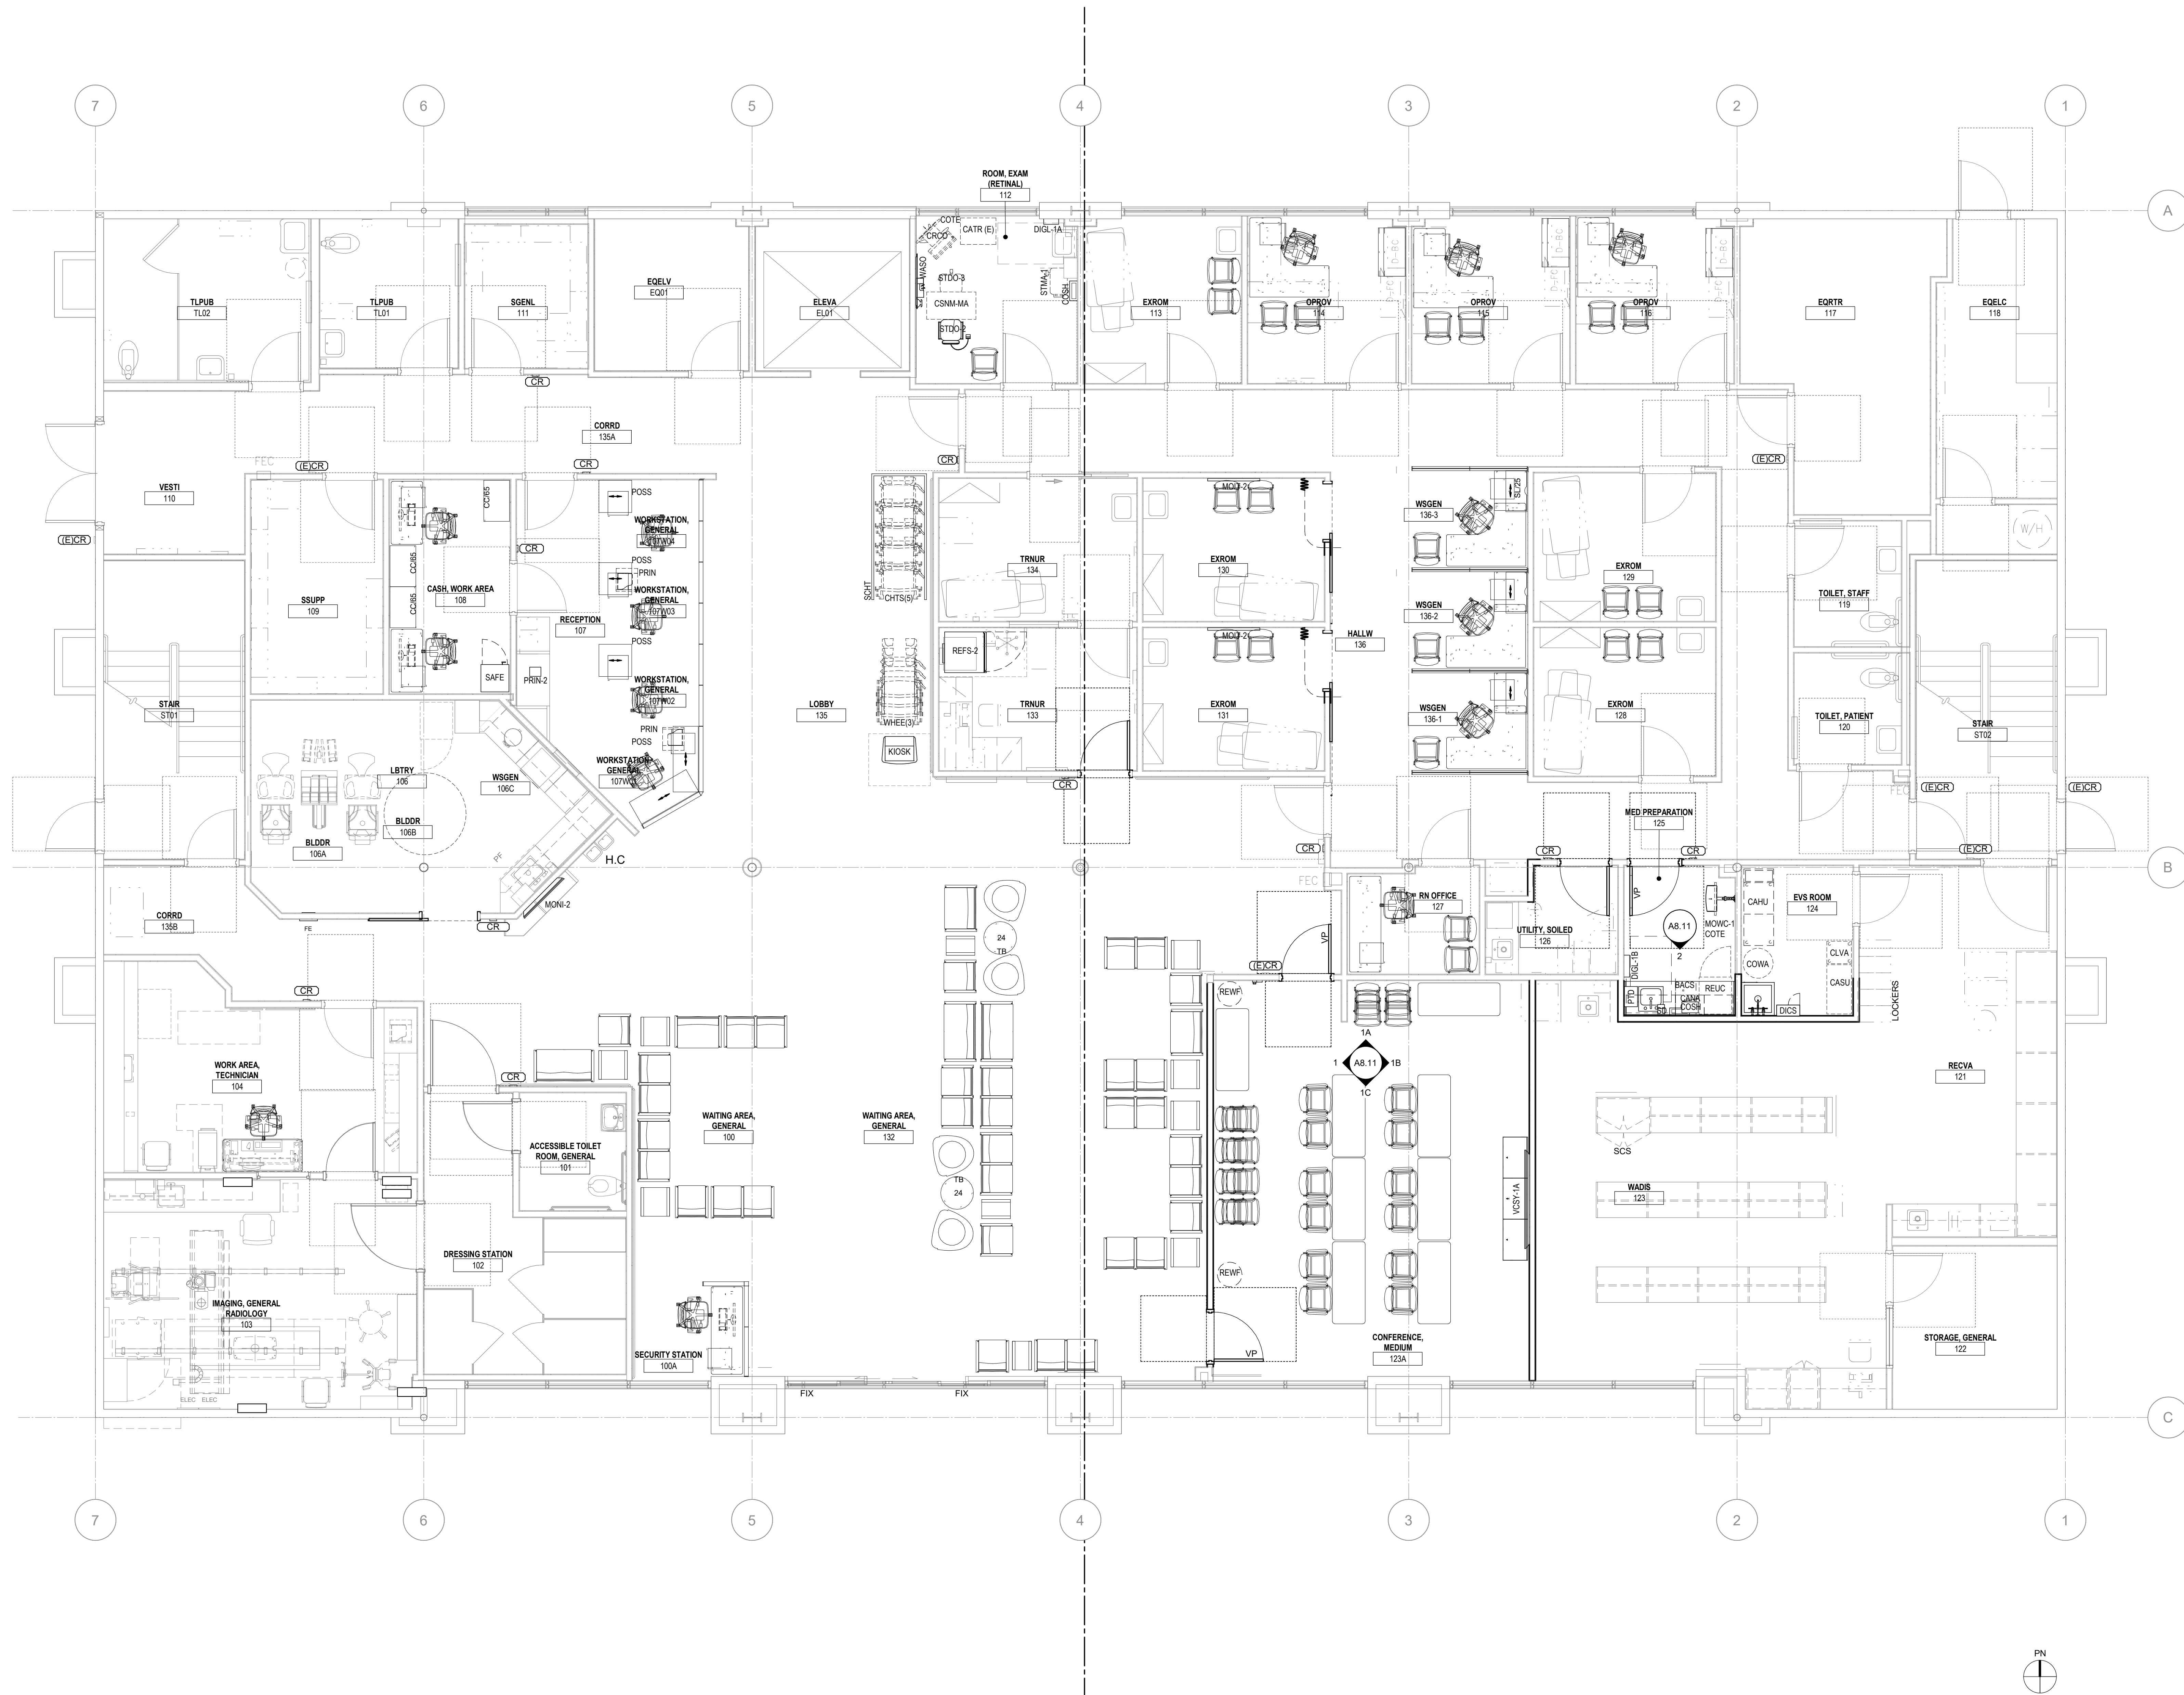

KAISER PERMANENTE®

National Facilities Services
Post Office Box 12916
Oakland, California 94604

HMC Architects

1152133-000

3546 CONCOURS STREET
ONTARIO, CA 91764
909 989 9979 / www.hmcarchitects.com

ISSUE

DESCRIPTION	DATE
-------------	------

KEYNOTES:

AGENCY
APPROVAL:

The type of approval to be issued by
The Office of Statewide Health and Planning Department
for this project is:

FACILITY:
KAISER ONTARIO MEDICAL CENTER
11911 CENTRAL AVENUE
CHINO, CA 91710

PROJECT:
CHINO MOB RESTORATION PROJECT

SHEET NAME:
FLOOR 1 - EQUIPMENT & FURNITURE PLAN

CONSTRUCTION DOCUMENTS

FAC NO.: XXXXX	BLDG NO.: XXXXX
DATE: 12/04/20	CLIENT PROJ NO: 10082081

SHEET:

Q2.11.

PLEASE RECYCLE